

A CIVIC ASSEMBLY PLAZA


ARC108: SEMESTER FINAL PROJECT
INSTRUCTOR: Mariah Smith

This project explores civic architecture as an active system that guides movement and shapes public experience. Derived from an analysis of circulation and visual cues, the design organizes a plaza through a structured spatial framework. Columns and vertical elements are used to direct flow, frame views, and create an immersive sequence of spaces, shifting civic architecture from static form to dynamic interaction.

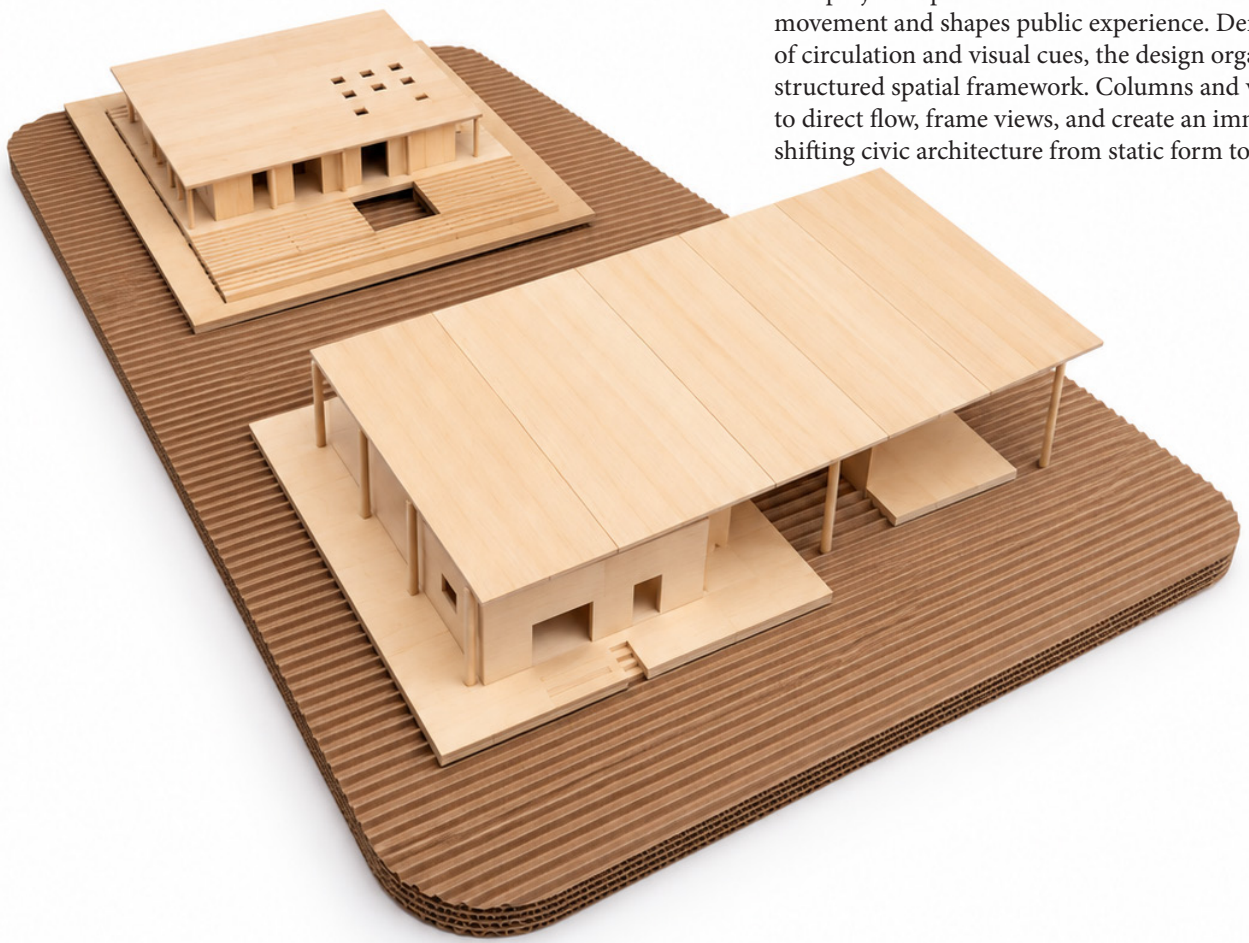


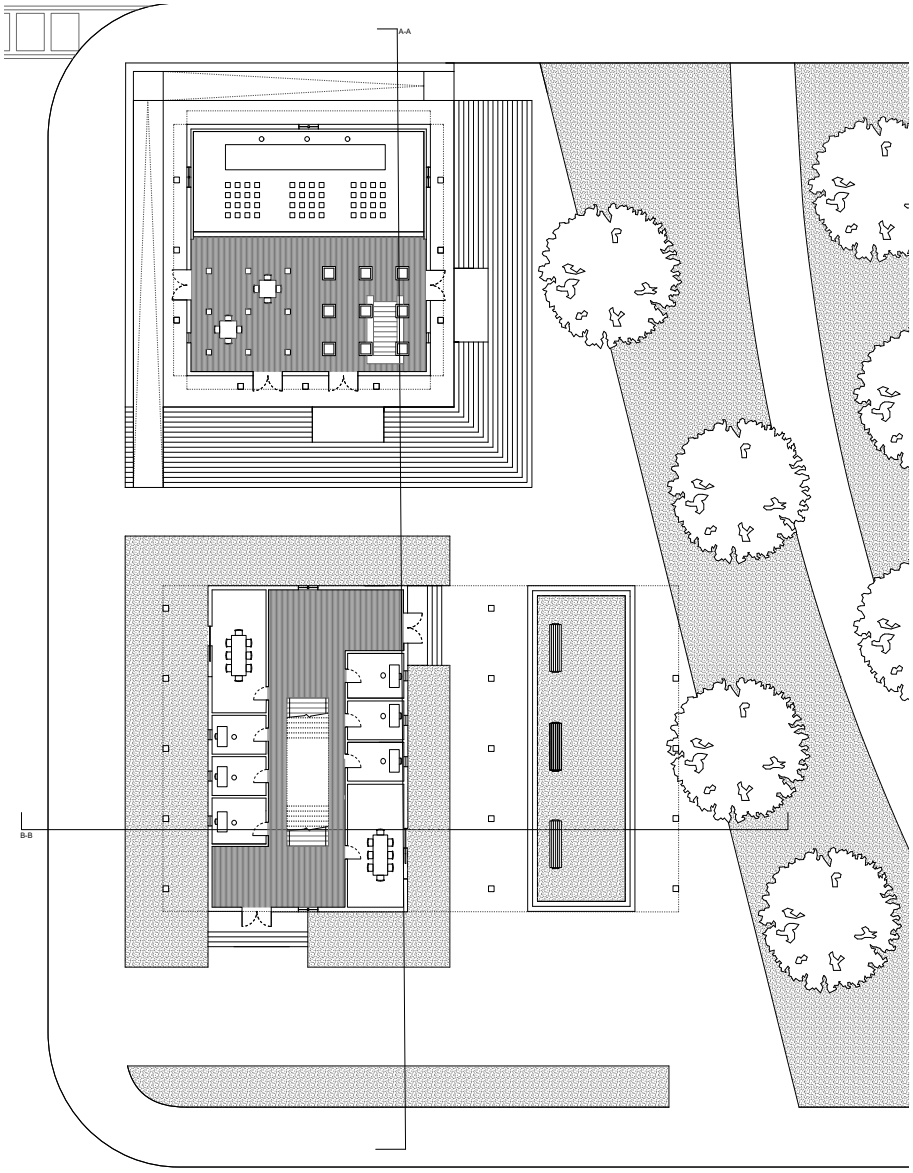

Ground Floor Plan - 1/8” = 1’0”

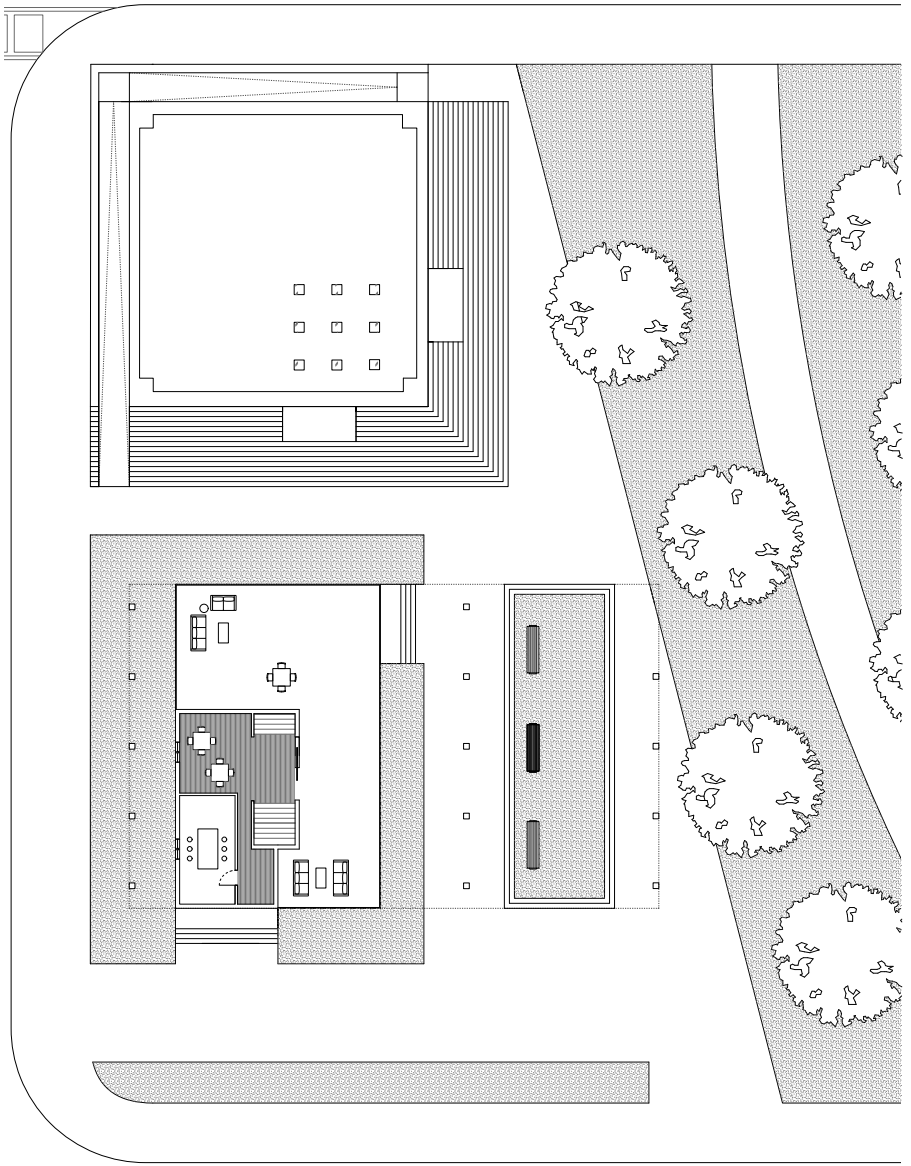


Second Floor Plan - 1/8” = 1’0”

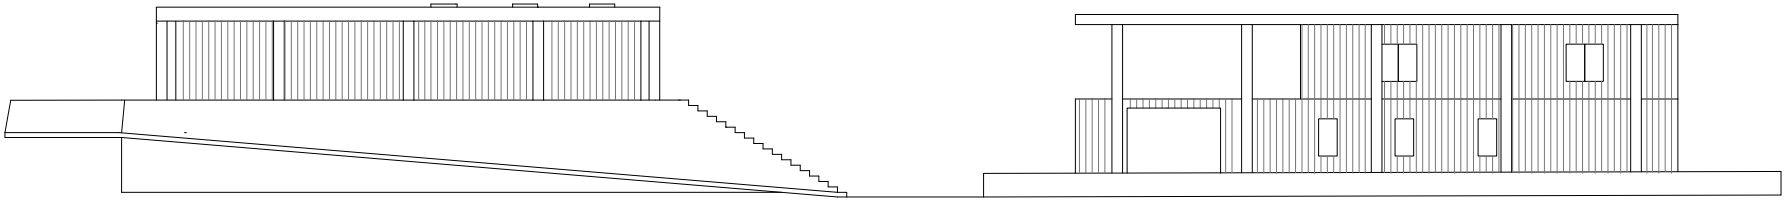


Elevation A-A




CORRESPONDING MODEL VIEW

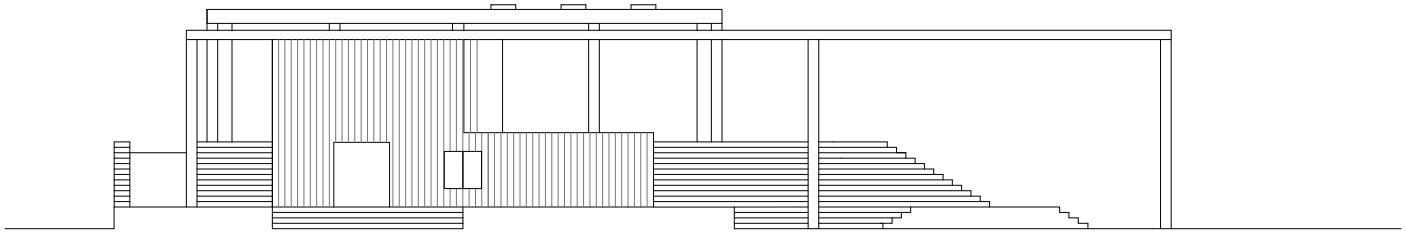


Elevation B-B

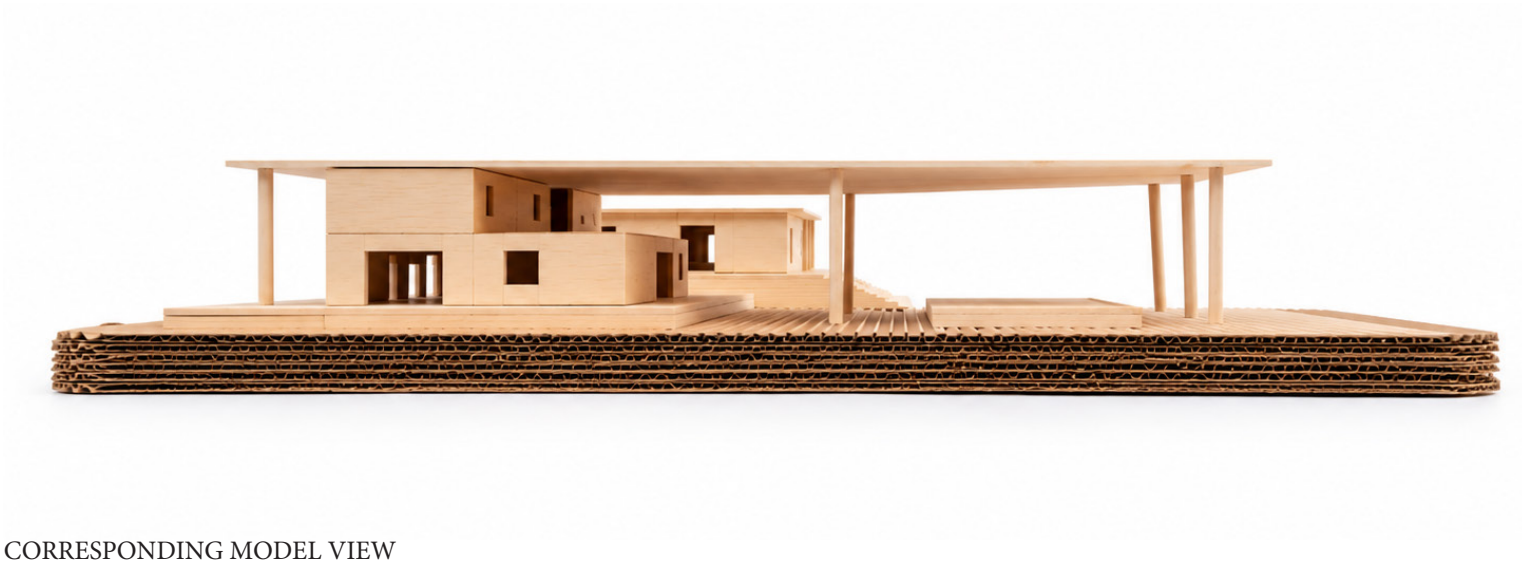


CORRESPONDING MODEL VIEW

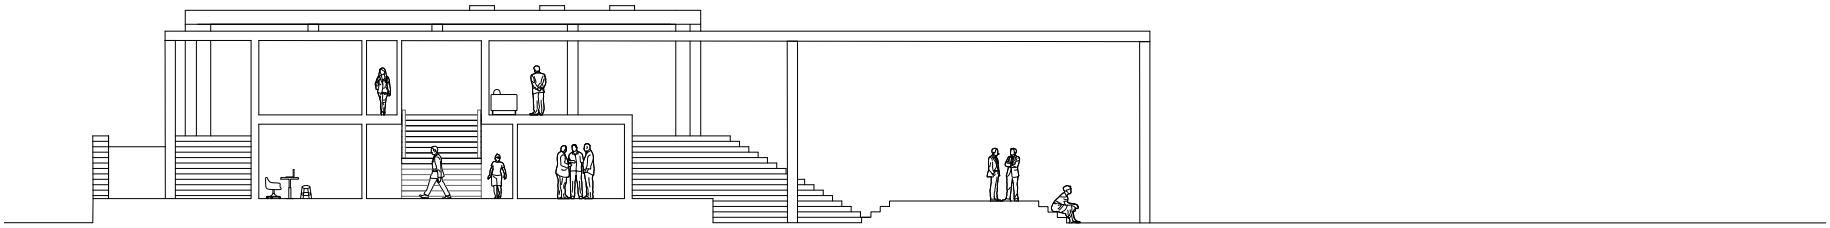


Section A-A

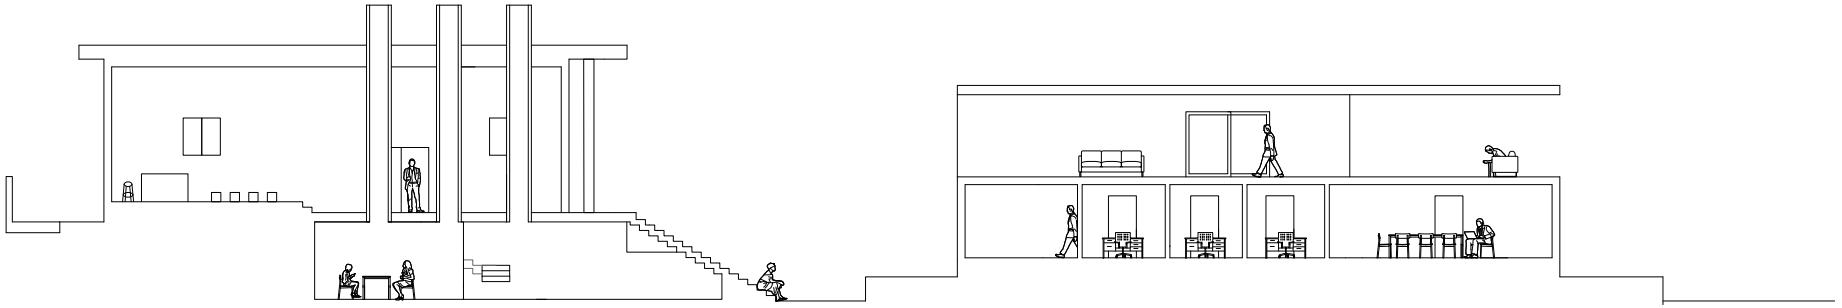

Section B-B

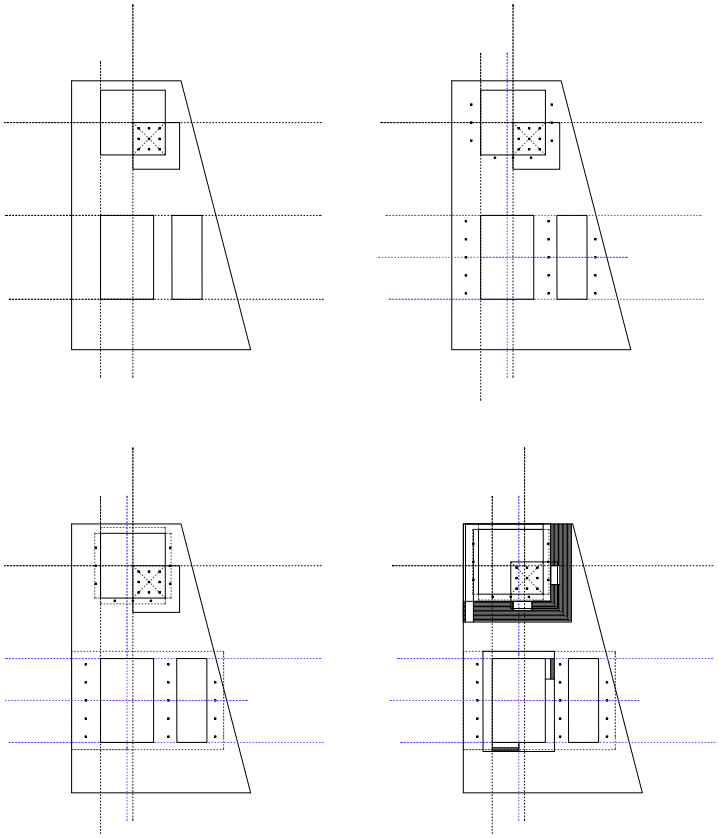

SYMMETRY/LOGIC DIAGRAMS

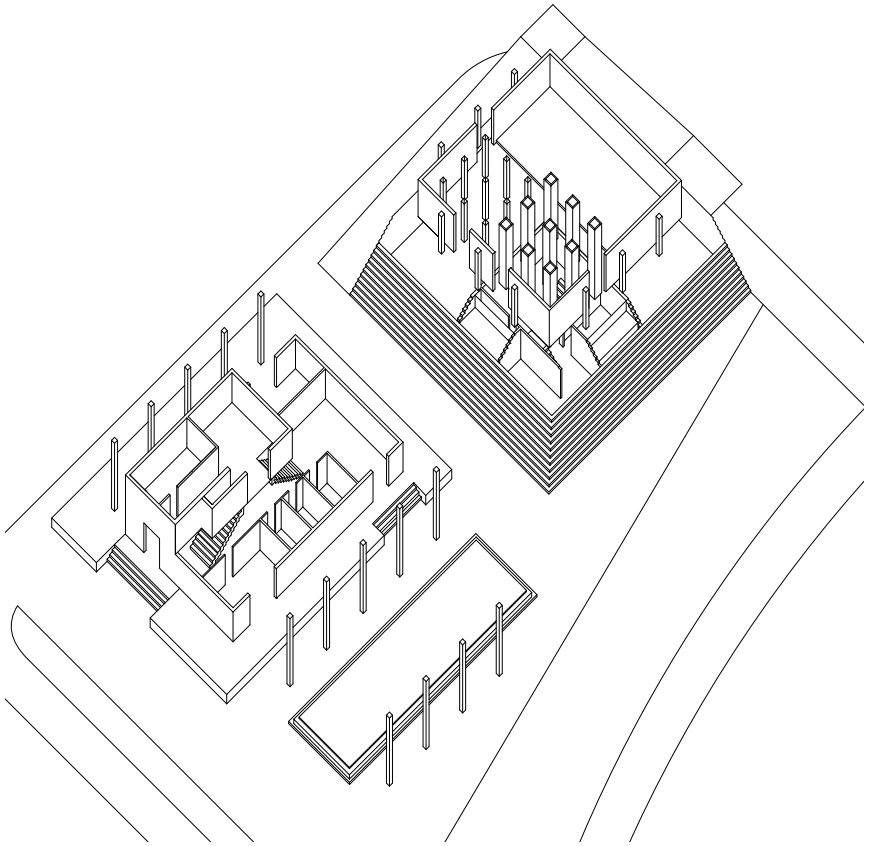

CIRCULATION OBLIQUE